




Réseaux			Nommage des systèmes
général	dalle / entree	plafond	
			RÉSEAU EAU DE CHAUFFAGE MANT ALLER
			RÉSEAU EAU DE CHAUFFAGE MANT RETOUR
			RÉSEAU EAU DE CHAUFFAGE ELEM ALLER
			RÉSEAU EAU DE CHAUFFAGE ELEM RETOUR
			RÉSEAU EAU DE CHAUFFAGE PERI ALLER
			RÉSEAU EAU DE CHAUFFAGE PERI RETOUR
			RÉSEAU EAU DE CHAUFFAGE CTA ALLER
			RÉSEAU EAU DE CHAUFFAGE CTA RETOUR
Equipements			Nommage des systèmes
			RACLETTE/A EAU
			NOUVRÉE DE DISTRIBUTION

o	27/03/2006	CDE	ML	Edition Originale
Indice	Date	Dessiné par	Verifié par	Description